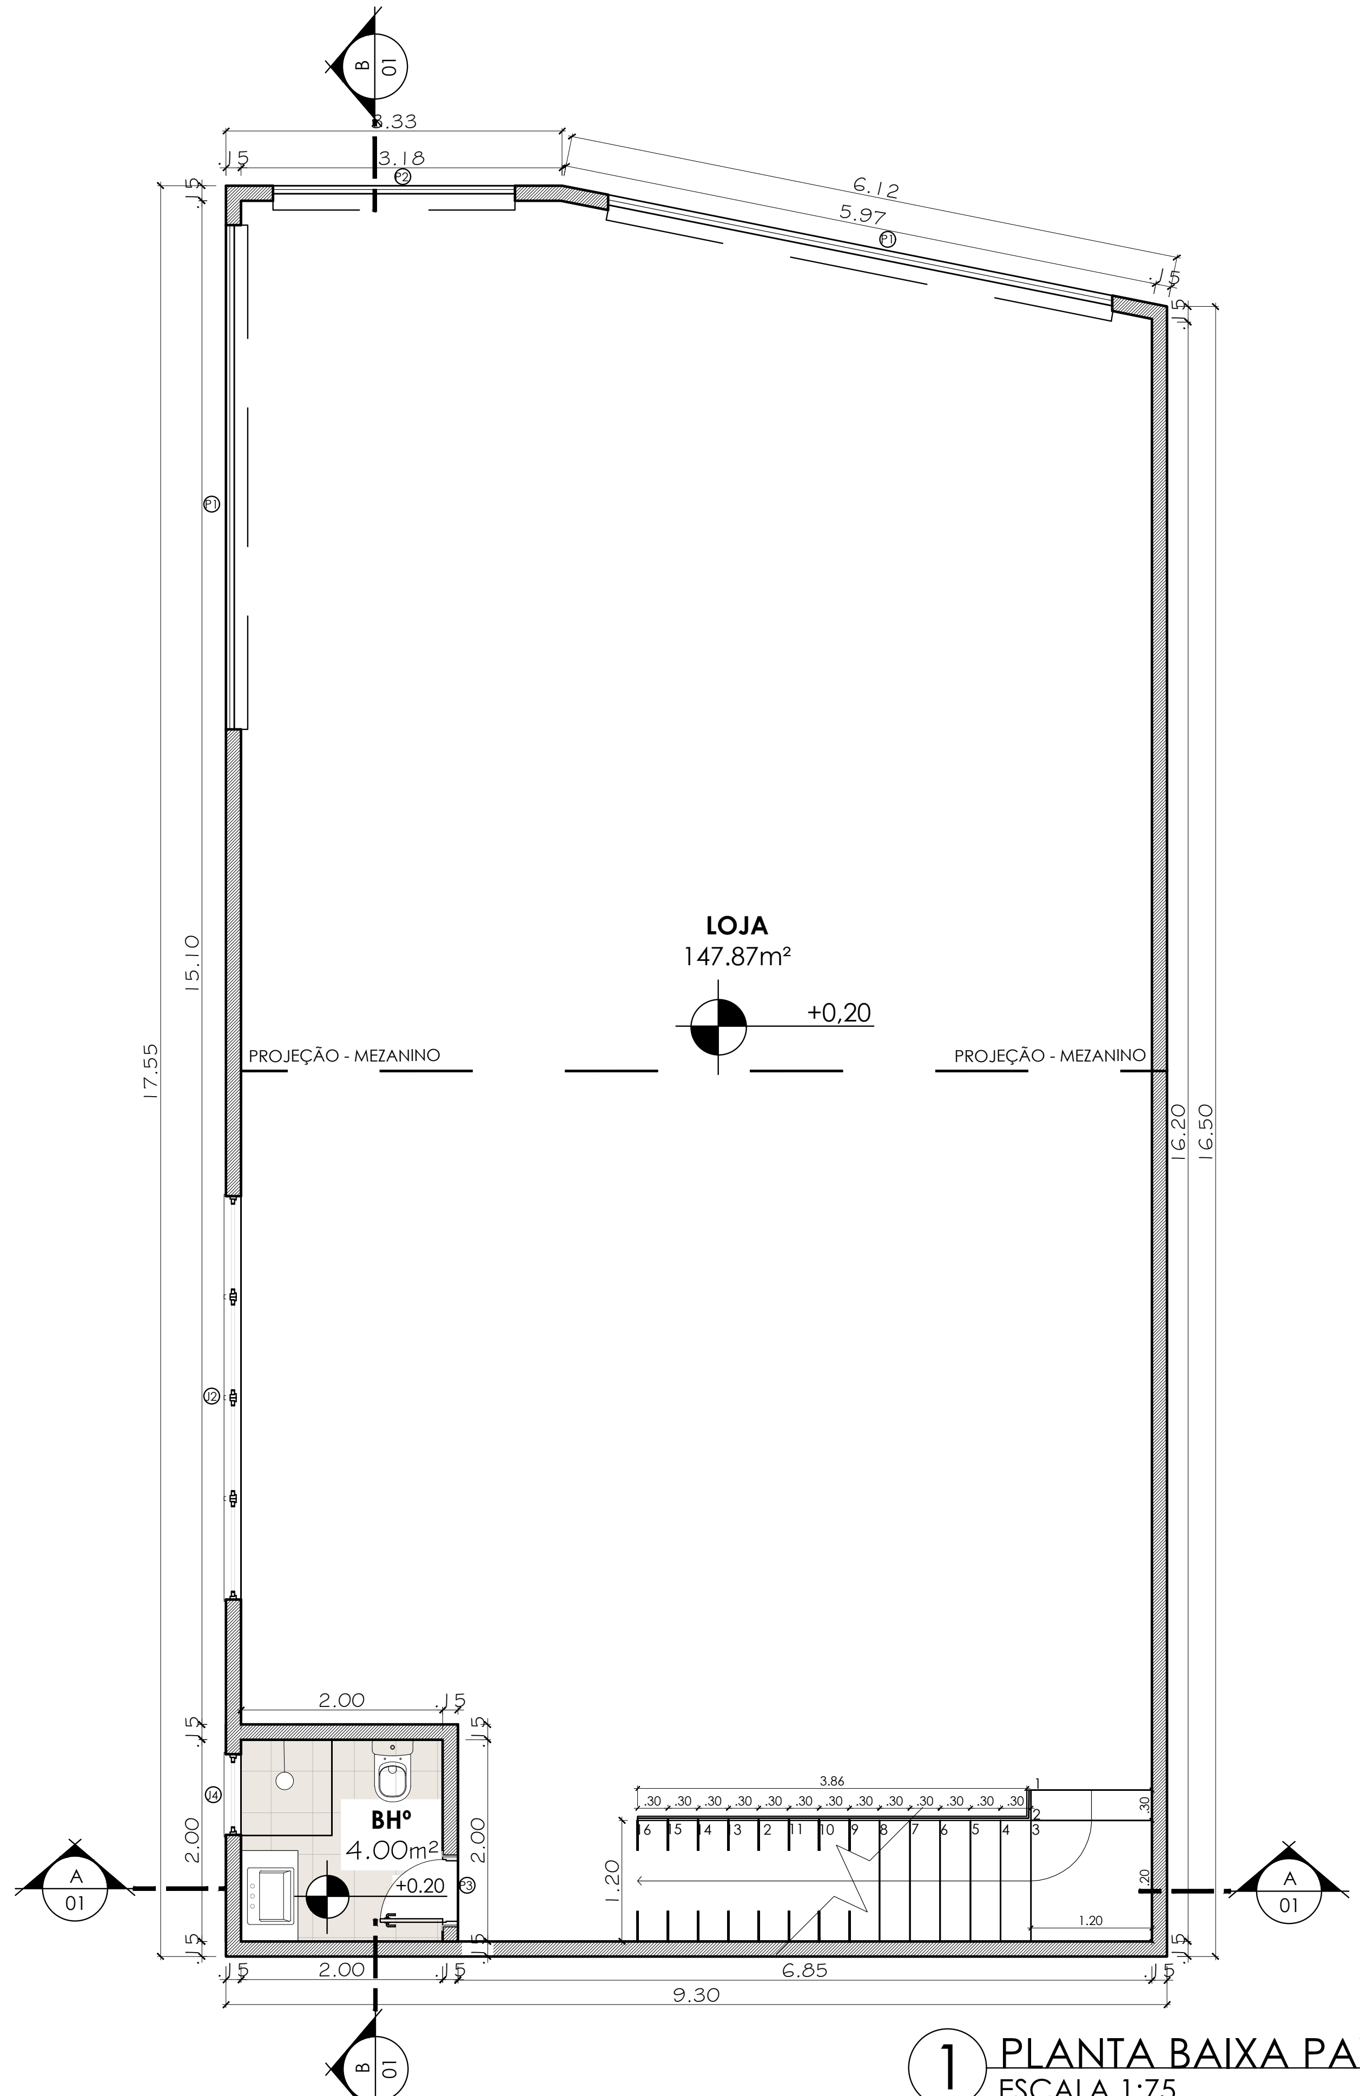

1 PLANTA BAIXA PAV- TÉRREO
ESCALA 1:75

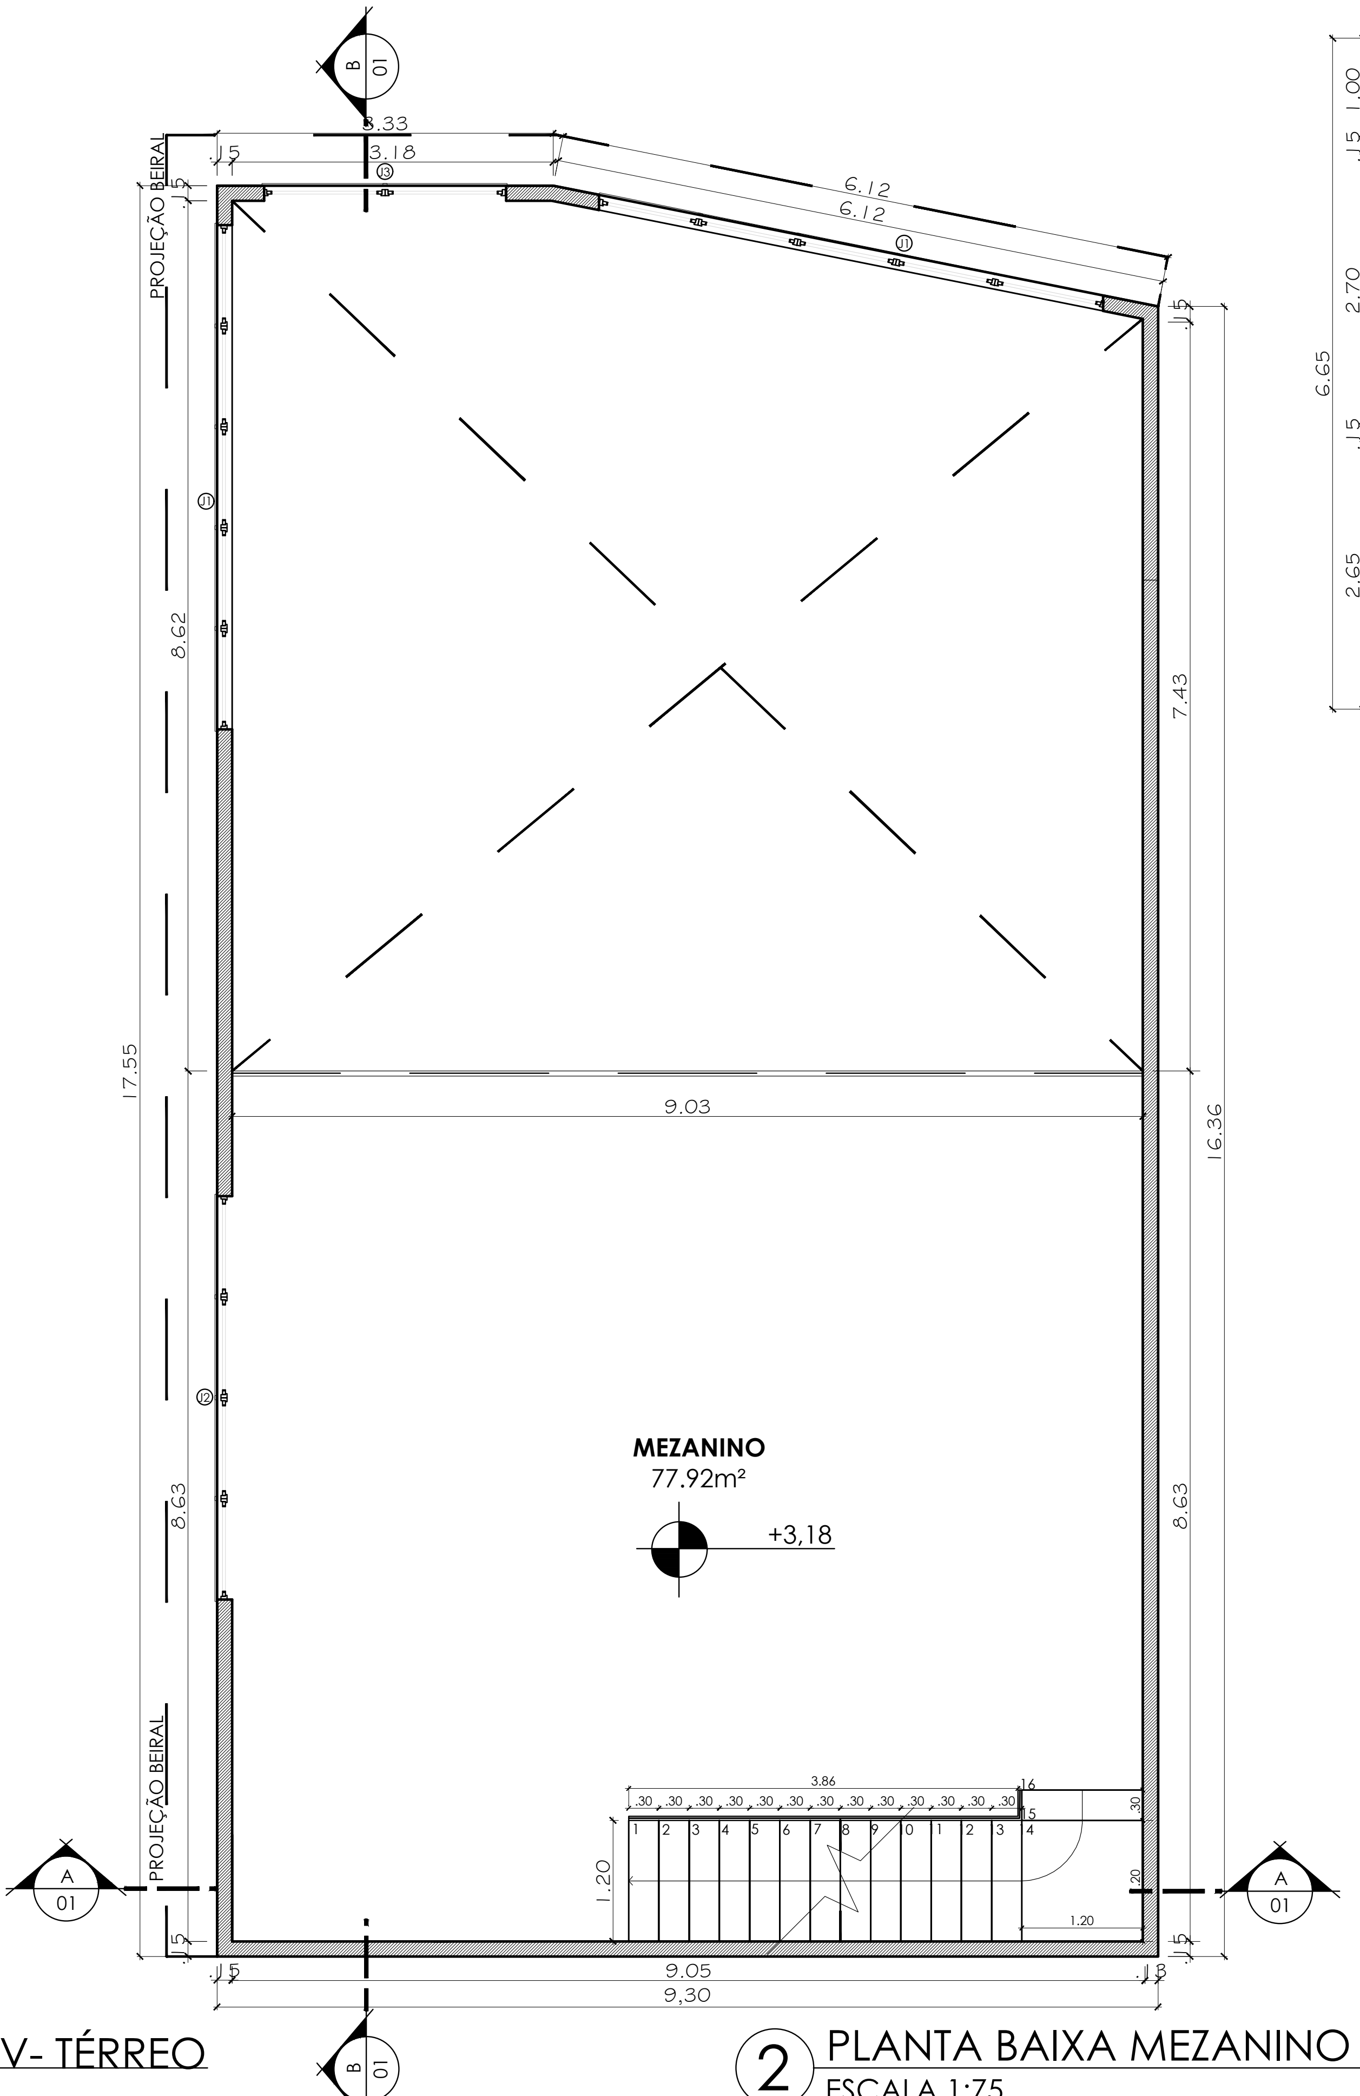

2 PLANTA BAIXA MEZANINO
ESCALA 1:75

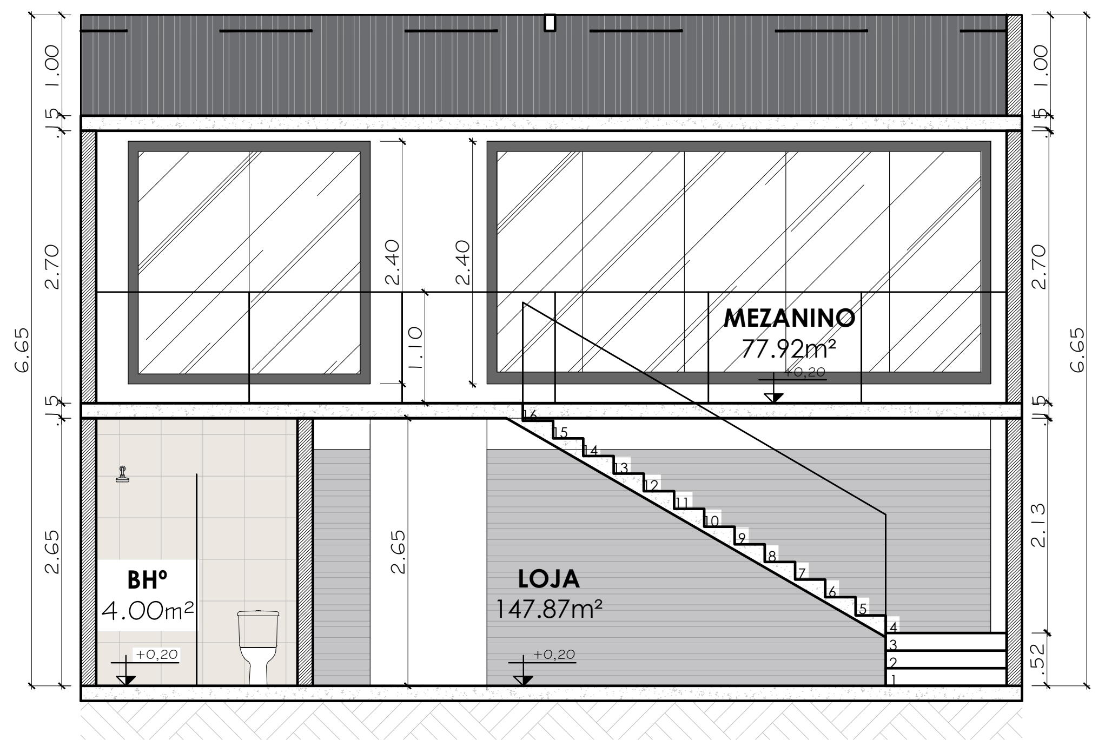

5 CORTE TRANSV. AA
ESCALA 1:75

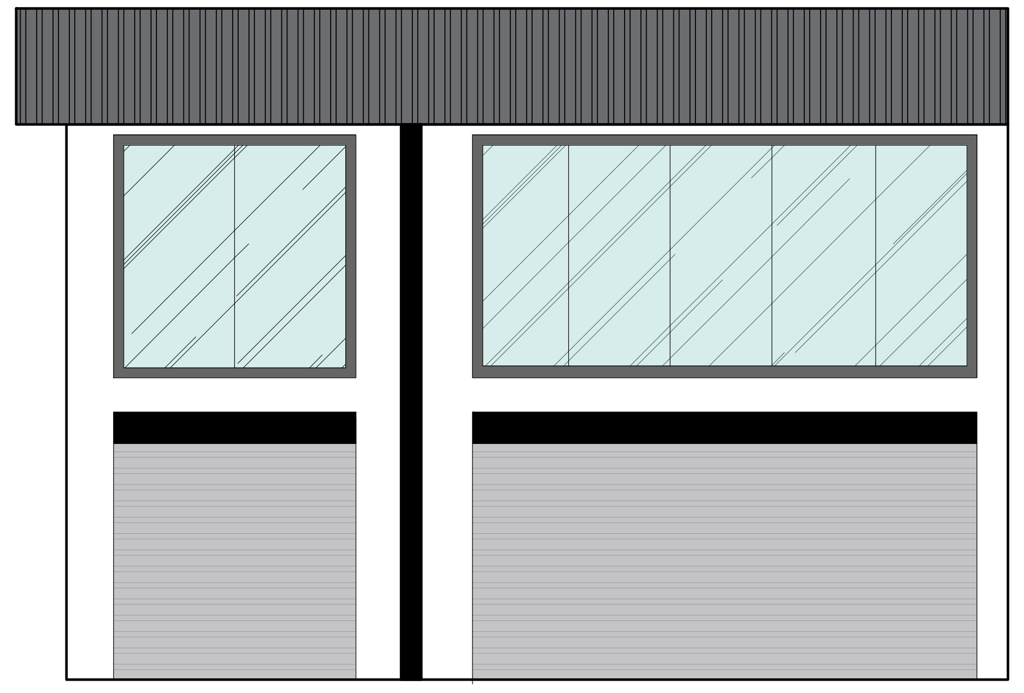

6 FACHADA P/ AV PRES. ROOSEVELT
ESCALA 1:75

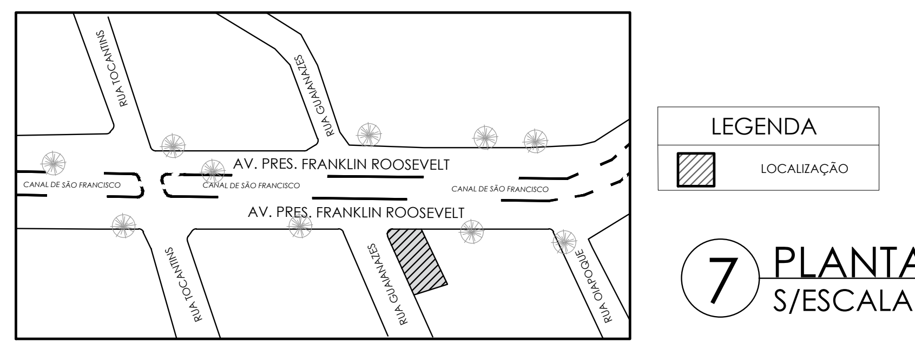

7 PLANTA DE LOCALIZAÇÃO
S/ESCALA

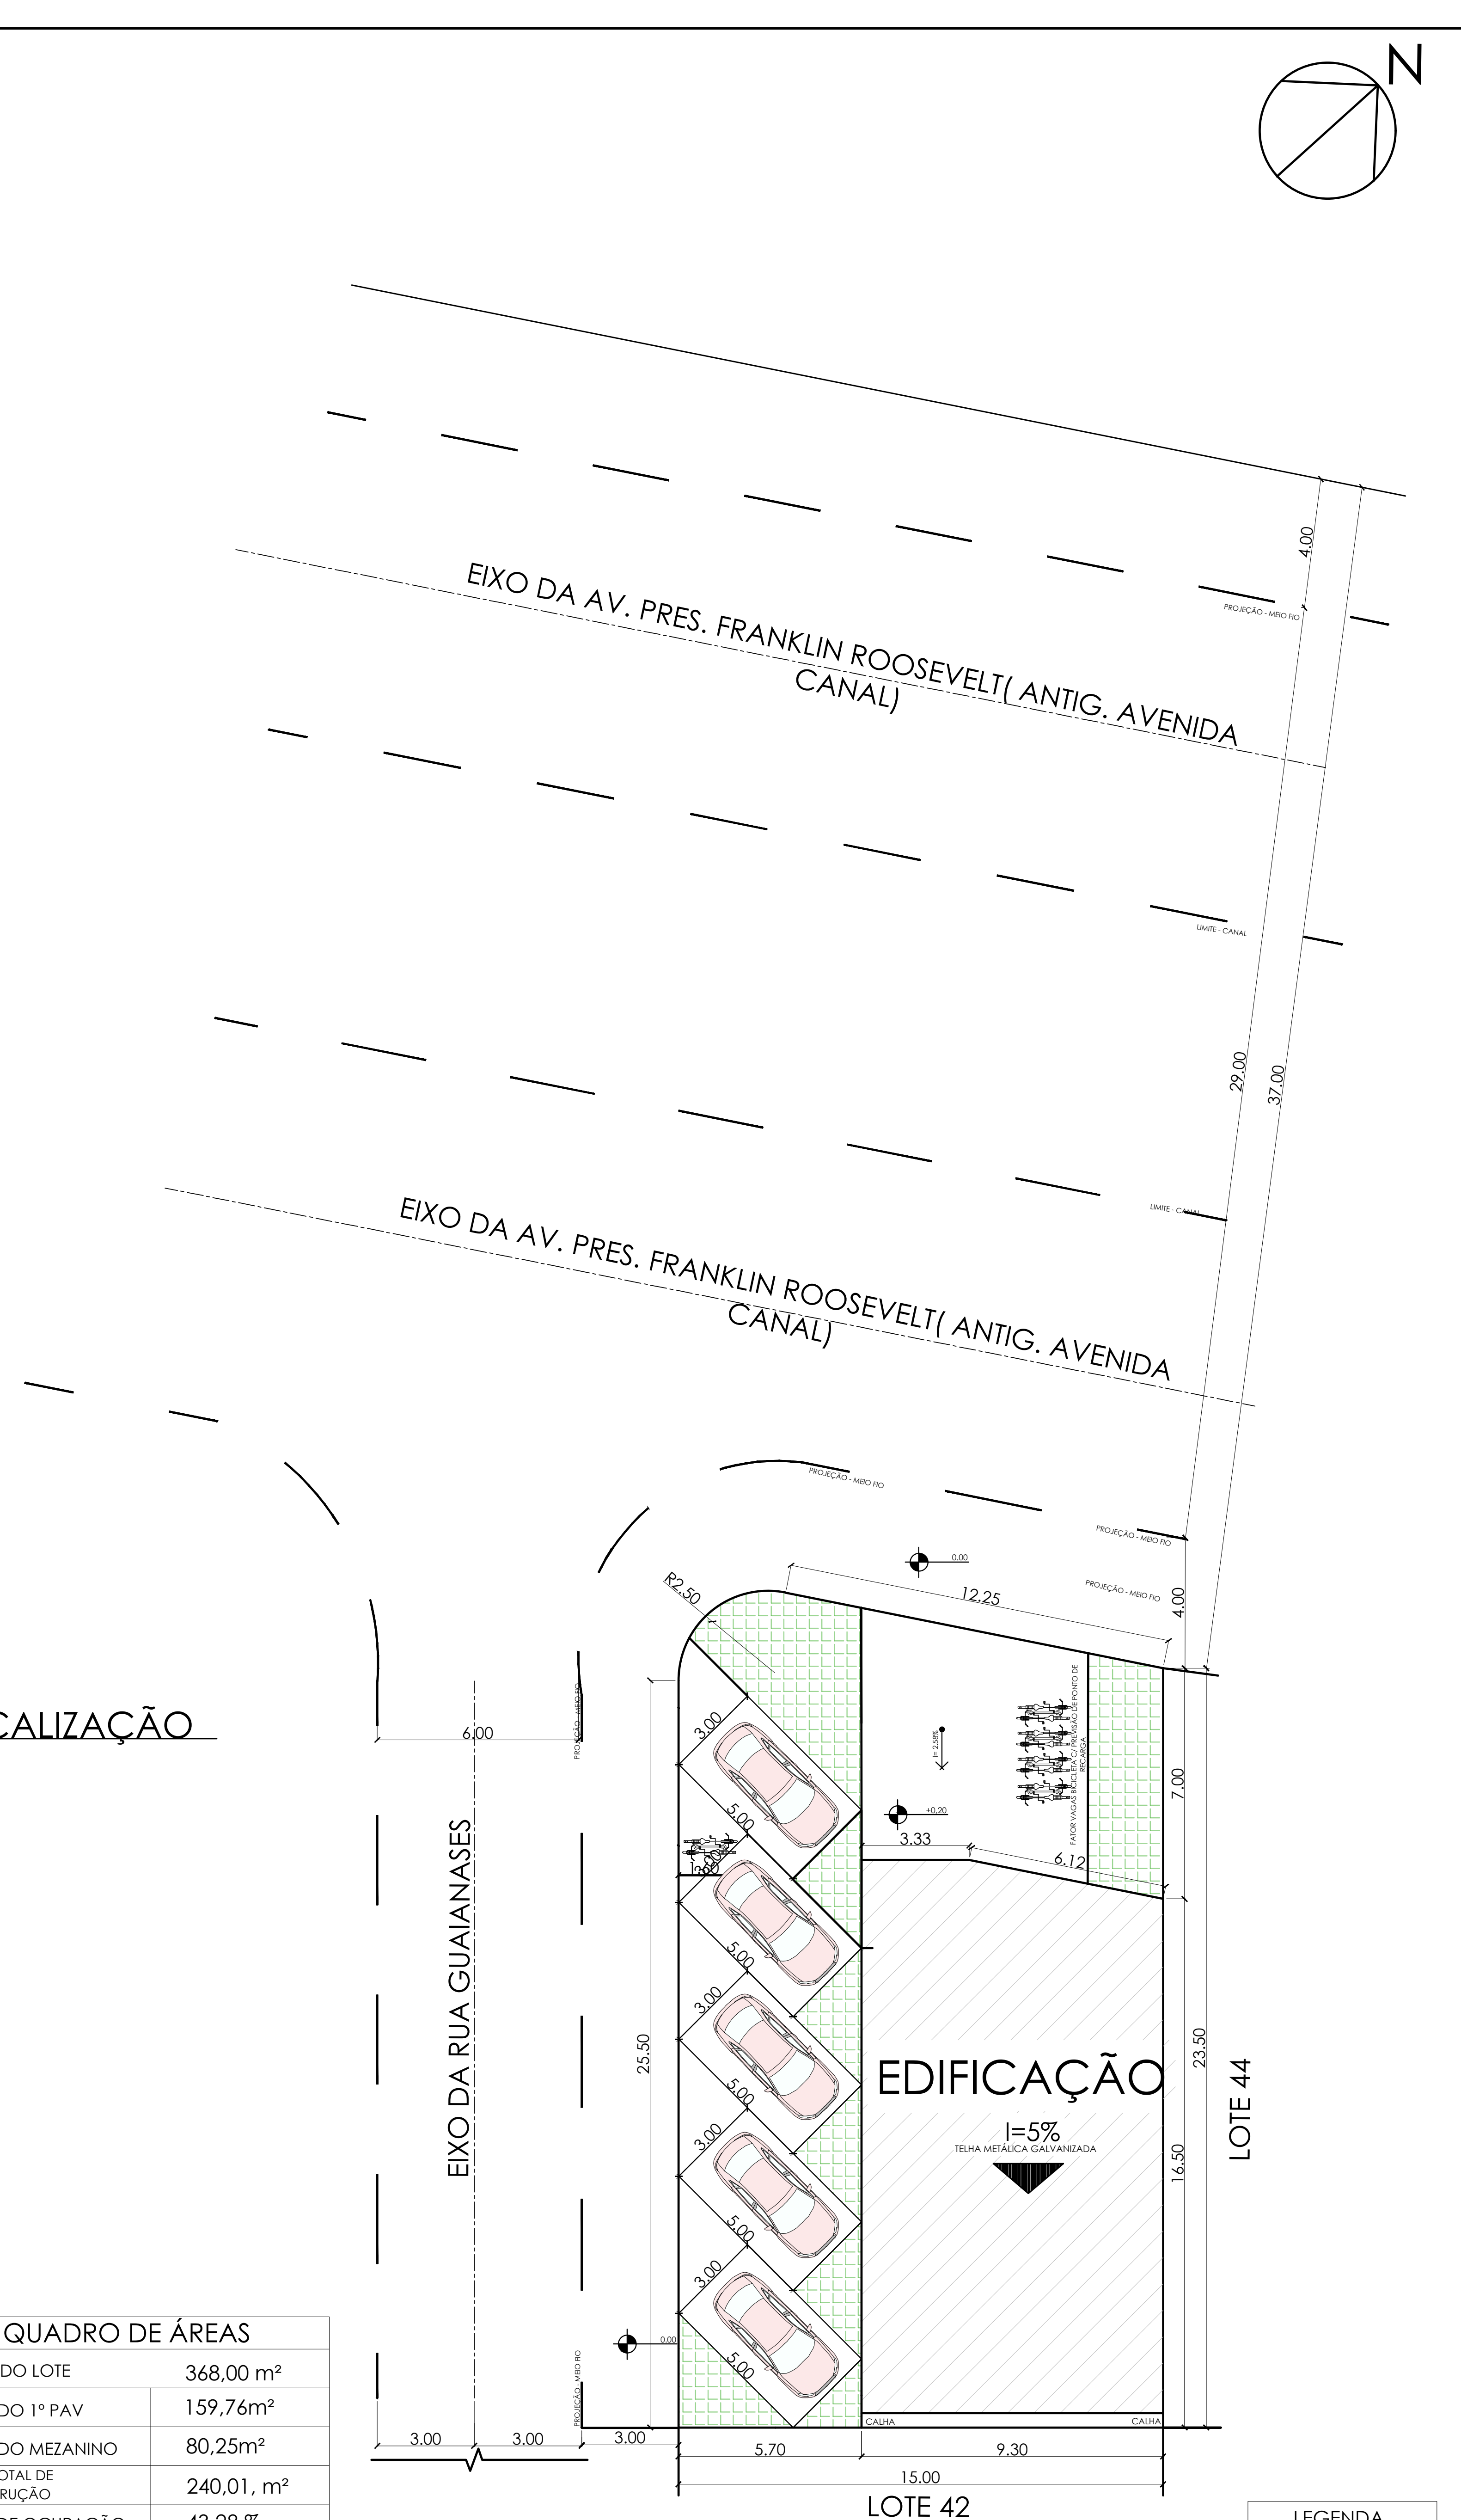

LEGENDA
🟩 ÁREA PERMEÁVEL

8 PLANTA DE SITUAÇÃO
ESC: 1:200

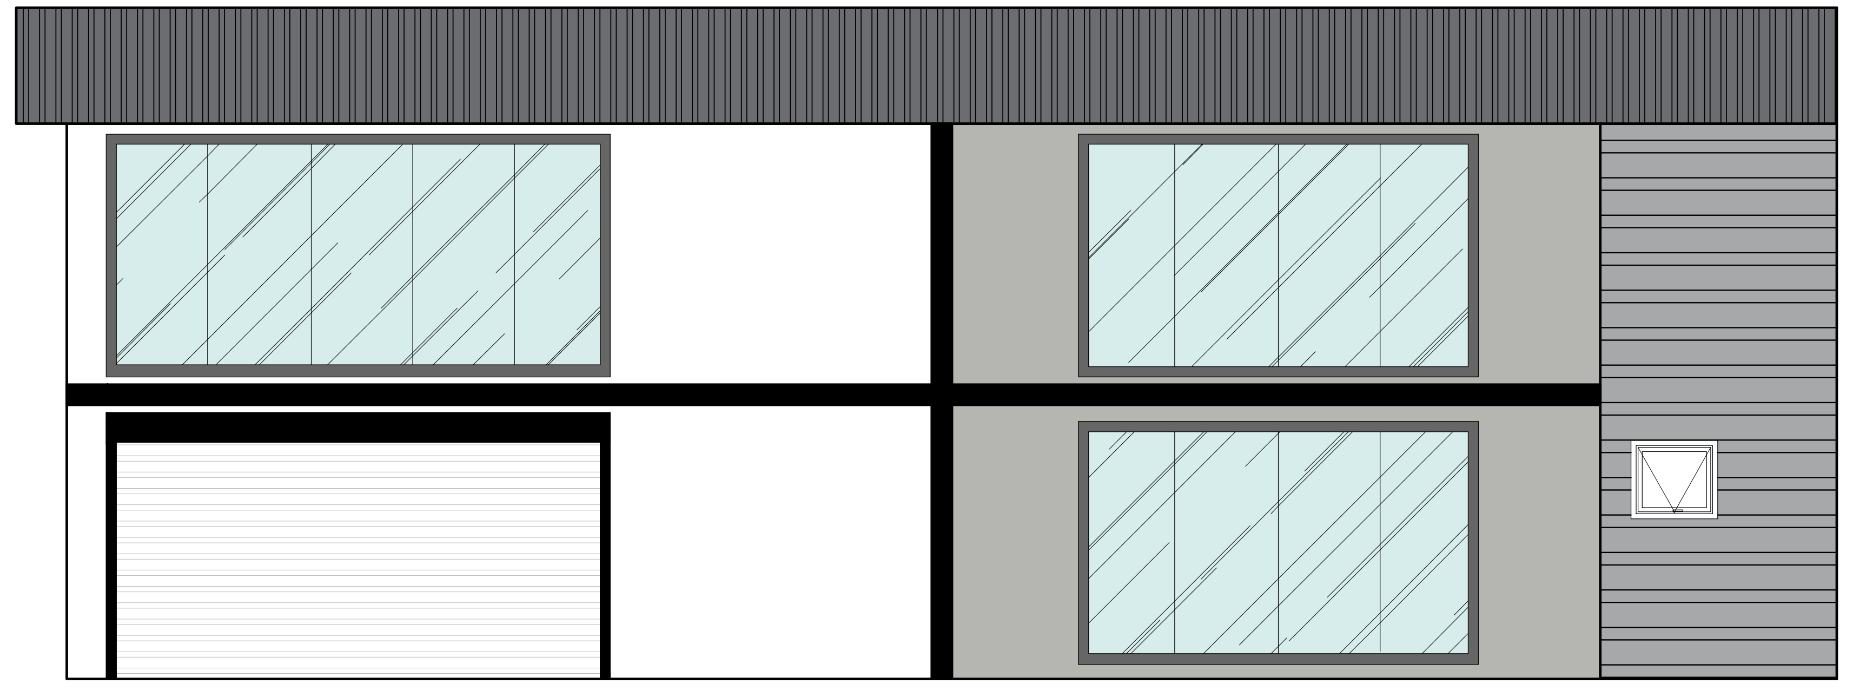

3 FACHADA P/ RUA GUAIANAZES
ESCALA 1:75

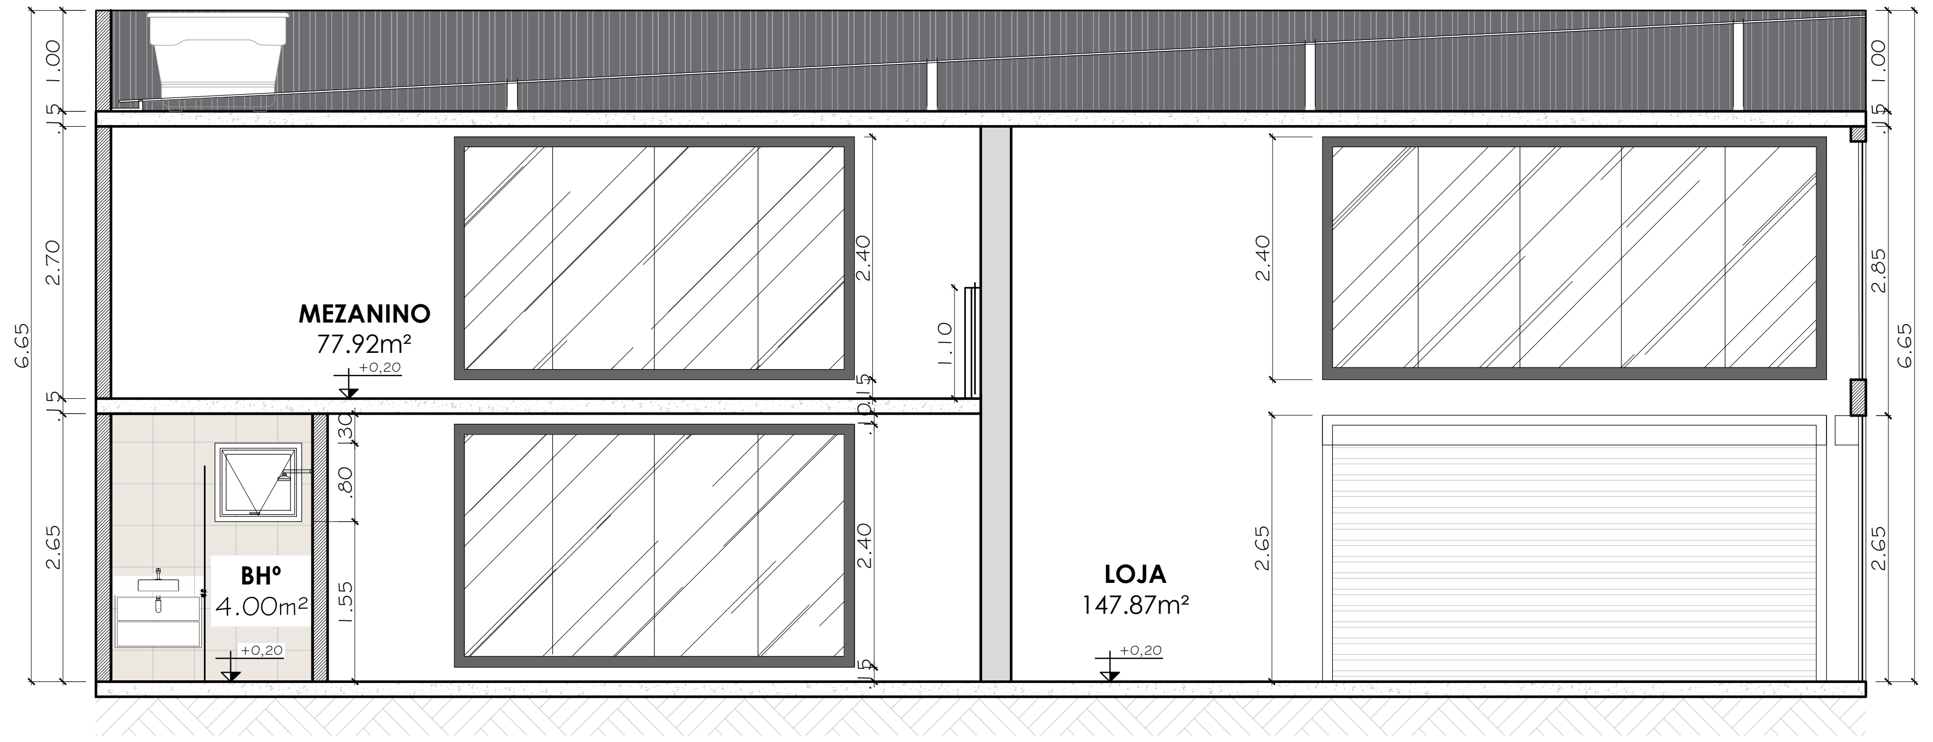

4 CORTE LONDITUDINAL BB
ESCALA 1:75

QUADRO DE ÁREAS	
ÁREA DO LOTE	368,00 m²
ÁREA DO 1º PAV	159,76m²
ÁREA DO MEZANINO	80,25m²
ÁREA TOTAL DE CONSTRUÇÃO	240,01, m²
TAXA DE OCUPAÇÃO	43,28 %
TX PERMEABILIDADE	20,01 %

QUADRO DE ESQUADRIAS

NOME	DESCRIÇÃO	TIPO	DIMENSÕES	PEITORIL
P1	PORTA EM ESQUADRIA EM ALUMÍNIO	ROLANTE	5.00 x 2,65	—
P2	PORTA EM ESQUADRIA EM ALUMÍNIO	ROLANTE	2,00 x 2,65	—
P3	PORTA EM ESQUADRIA EM ALUMÍNIO	GIRO	0,70 x 2,10	—
J1	JANELA EM ESQUADRIA EM ALUMÍNIO + VIDRO TEMPERADO	CORRER	5,00 x 2,00	—
J2	JANELA EM ESQUADRIA EM ALUMÍNIO + VIDRO TEMPERADO	CORRER	4,00 x 2,00	—
J3	JANELA EM ESQUADRIA EM ALUMÍNIO + VIDRO TEMPERADO	MAXIM-AR	2,00 x 2,40	—
J4	JANELA EM ESQUADRIA EM ALUMÍNIO + VIDRO TEMPERADO	MAXIM-AR	0,80 x 0,80	—

PREFEITURA MUNICIPAL DE NITERÓI
SECRETARIA DE URBANISMO

ZONEAMENTO	MACROÁREA	TERRITÓRIO	ZONA DE USO
	MACROAREA DE URBANIZAÇÃO CONSOLIDADA	XXXXXXXXXX	ZUM + 4

	FACHADA ATIVA	COEFICIENTE DE APROVEITAMENTO	AFASTAMENTOS (m) FRENTE	LATERAIS	FUNDO	TAXA DE OCUPAÇÃO
QUADRO III	OBRIGATÓRIO	1,0	7.00	3,00	-	53,02%

	TIPO DE USO	PORTE	TIPO DE VIA	CLASSIFICAÇÃO
QUADRO IV	NÃO RESIDENCIAL		EIXO	XXXXXXXXXXX

	TESTADA A TESTADA	CAIXA DE ROLAMENTO	PASSEIOS (PAR / ÍMPAR)	RECUOS PAR	
QUADRO V	37	29	4,00 ; 3,00	XXX	

	VAGAS DE VEÍCULOS	MÍNIMO DE VAGAS DE BICICLETAS		FATOR DE PLANEJ. (Fp)		FATOR DE INTERESSE SOCIAL (Fs)
QUADRO VI	5	XXXXXXXXXXX	QUADRO VII-A	XXXXXXXXXXX	QUADRO VII-B	XXXXXXXXXXX

PARÂMETROS QUALIFICADORES DE OCUPAÇÃO DO SOLO
- ☐ PERMEABILIDADE VISUAL
- ☐ USO MISTO
- ☒ FACHADA ATIVA
- ☐ FRUIÇÃO PÚBLICA
- ☒ VAGAS PARA BICICLETAS

PARÂMETROS QUALIFICADORES DO MEIO AMBIENTE
- ☒ TAXA DE PERMEABILIDADE (TP)
- ☐ TELHADO VERDE
- ☐ FACHADA VERDE
- ☐ TAXA DE PRESERVAÇÃO DA VEGETAÇÃO (TPV)
- ☐ SISTEMA DE RETARDAMENTO DO ESCOAMENTO DE ÁGUAS PLUVIAIS
- ☐ ARBORIZAÇÃO URBANA
- ☐ SISTEMA DE REUSO DA ÁGUA

OBSERVAÇÕES

TÍTULO
PROJETO PARA CONSTRUÇÃO DE EMPREENDIMENTO NÃO RESIDENCIAL

PRANCHA Nº
01

ENDEREÇO
AV. PRESIDENT FRANKLIN ROOSEVEL, ESQUINA COM RUA GUAIANAZES - Nº 32
BAIRRO DE SÃO FRANCISCO - MUNICÍPIO DE NITERÓI (RJ)

REGIÃO
PRAIAS DA BAÍA

PROPRIETÁRIO **FABIANO NADER DAMIÃO**
CPF: 639.018.387/91

AUTORIA DO PROJETO **PEDRO HENRIQUE COELHO GONÇALVES**
(CAU RJ A2783401)

RESPONSABILIDADE PELA EXECUÇÃO DA OBRA **PEDRO HENRIQUE COELHO GONÇALVES**
(CAU RJ A2783401)

USO EXCLUSIVO DA SMU

PROCESSO Nº
DATA: XX/XX/XXXX

APROVAÇÃO DO PROJETO
ANALISTA:
MATRÍCULA:
*VÁLIDO SOMENTE COM ASSINATURA DIGITAL PELO GOV.BR E QR CODE

PARECERES

ACEITE DE OBRAS
BOLETIM Nº:
DATA: XX/XX/XXXX